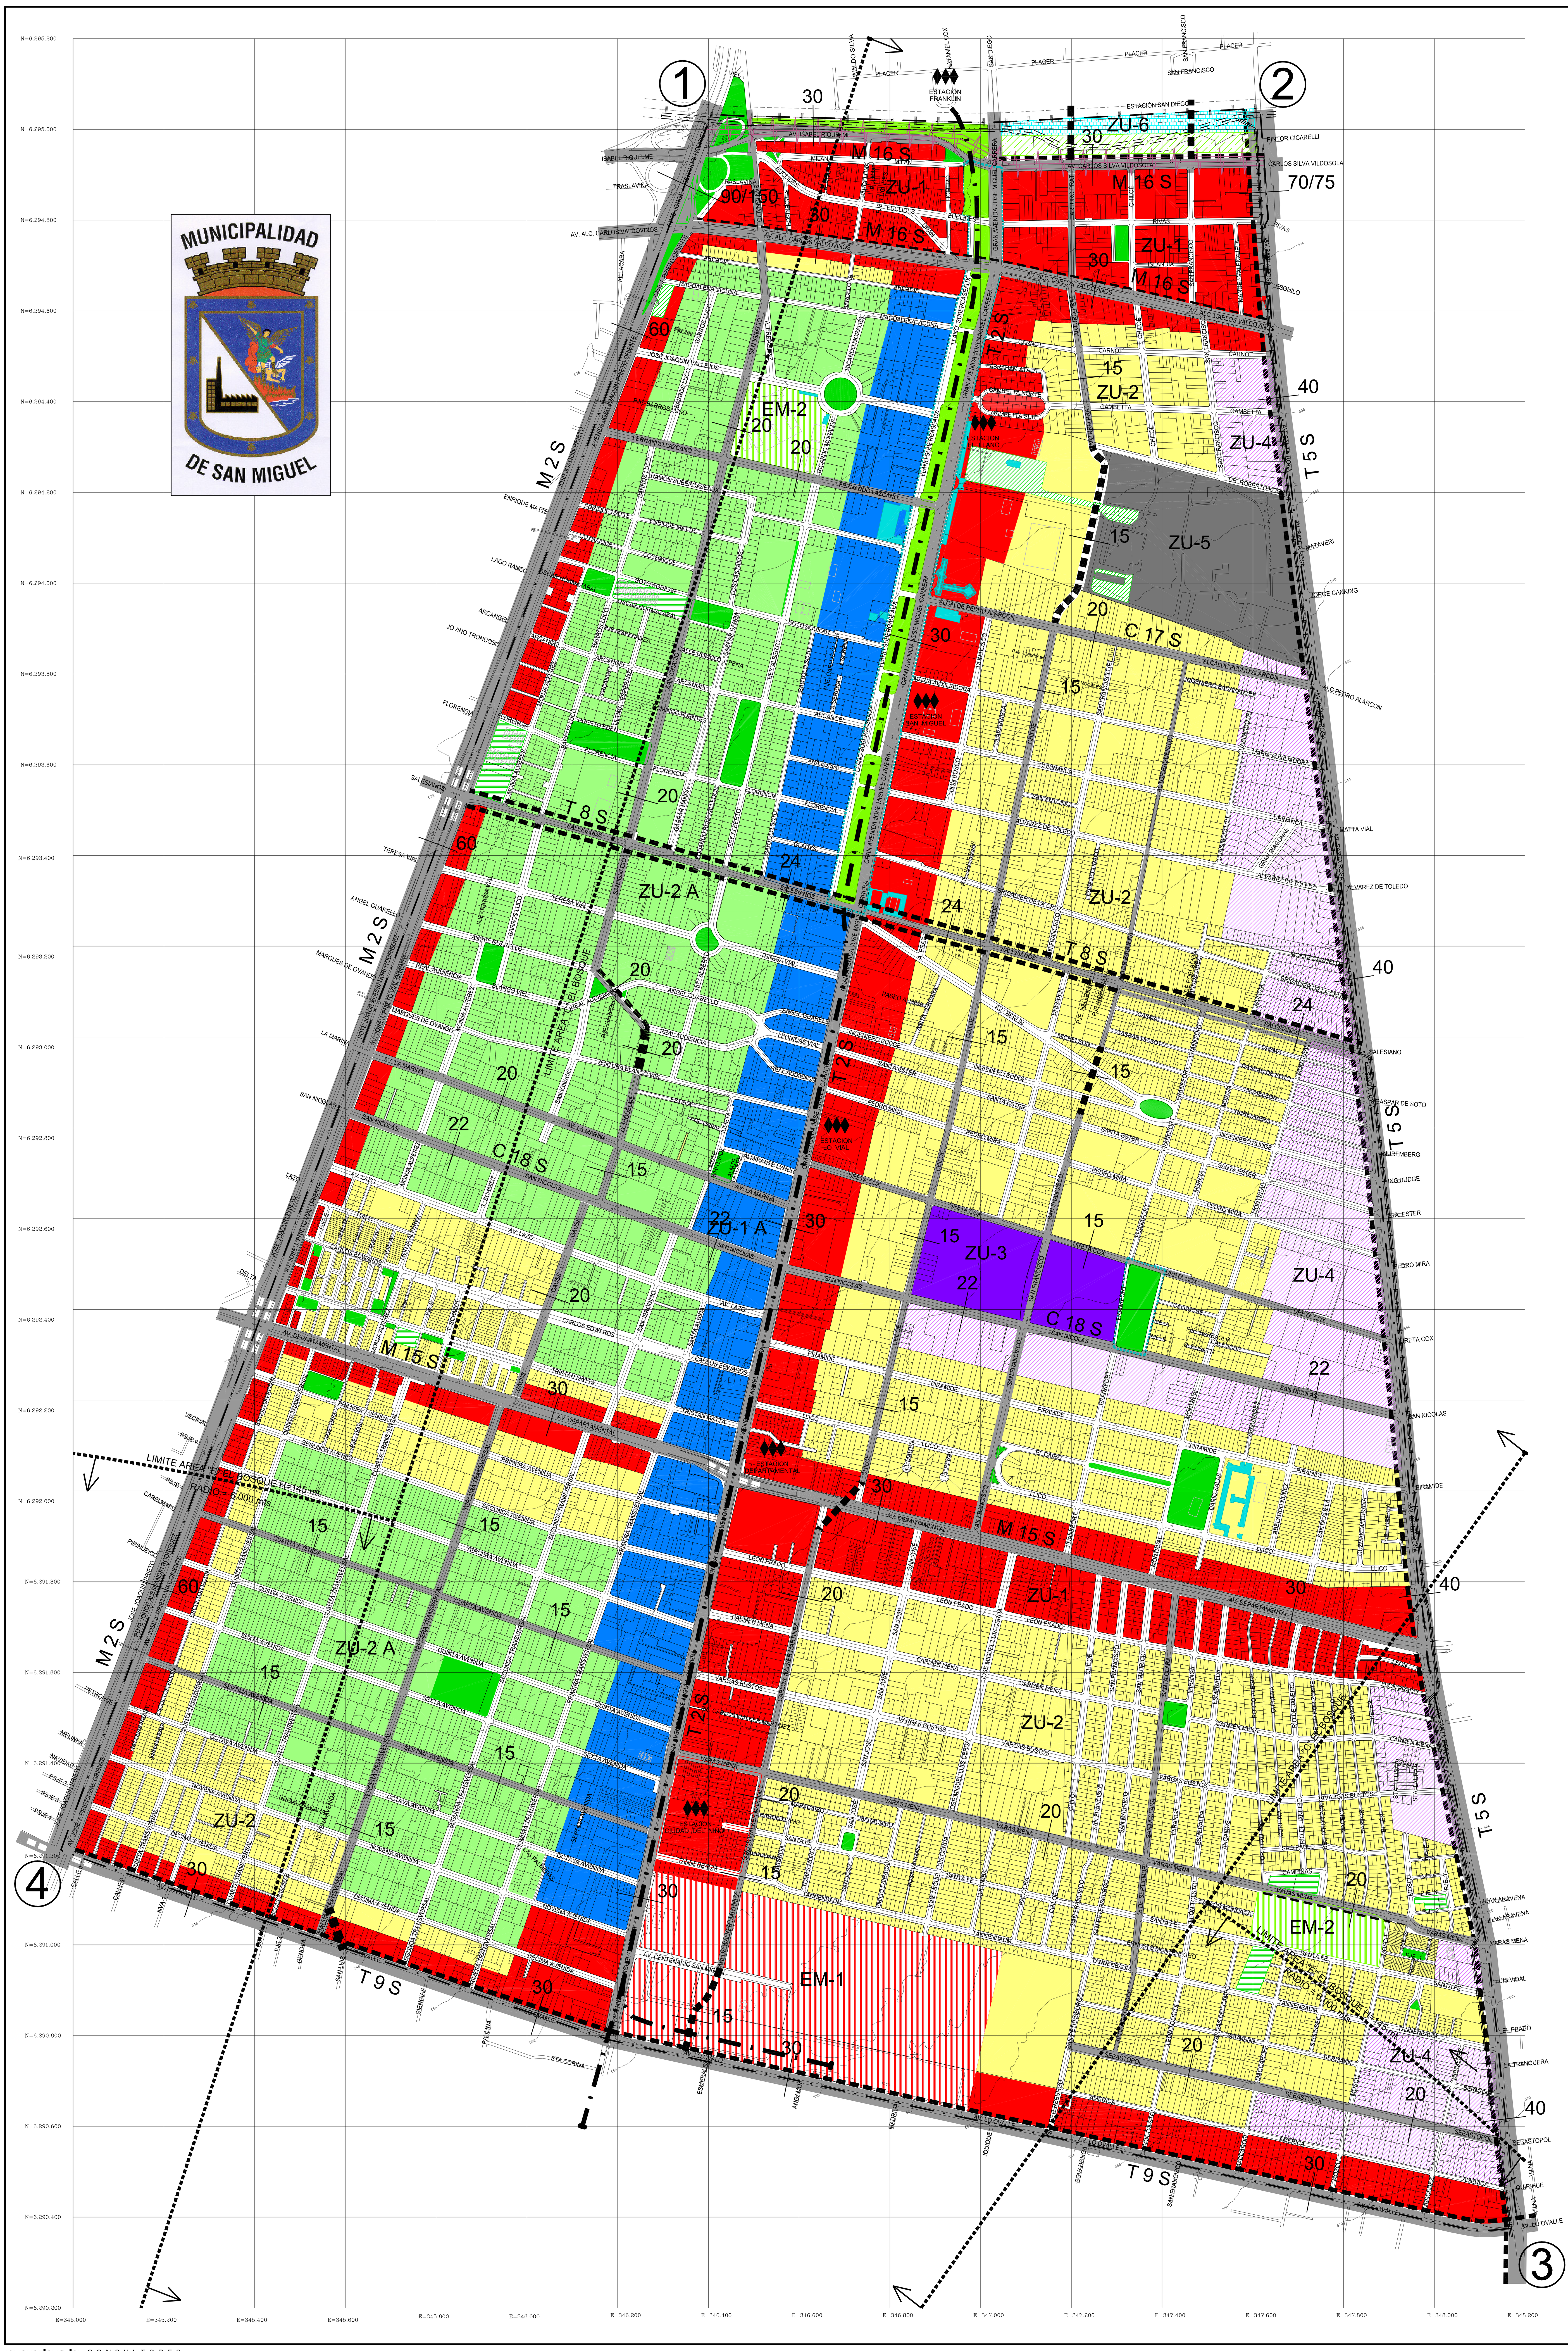


ecohab CONSULTORES

TITULO

PLAN REGULADOR COMUNAL DE SAN MIGUEL

TEMA

PLANO PRSM-3
ZONIFICACIÓN ENMIENDA

SIMBOLOGIA

ZONIFICACIÓN

- ZU-1 Comercial Preferente y Residencial
- ZU-1 A Comercial Preferente y Residencial
- ZU-2 Residencial de Renovación
- ZU-2 A Residencial de Renovación
- ZU-3 Industrial Exclusiva
- ZU-4 Industrial Mixta
- ZU-5 Equipamiento Regional de Salud
- ZU-6 Zona Ferroviaria

EQUIPAMIENTO Y ÁREAS VERDES, NIVEL METROPOLITANO E INTERCOMUNAL

- EM-1 Equipamiento Intercomunal
- EM-2 Equipamiento Recreacional y Deportivo
- EM-3 Áreas Verdes Existentes Intercomunales (Avenidas Parque)
- EM-4 Áreas Verdes Proyectas Intercomunales (Avenida Parque)

EQUIPAMIENTO Y ÁREAS VERDES, NIVEL COMUNAL

- EC-1 Equipamiento Recreacional y Deportivo
- EC-2 Áreas Verdes Comunales
- EC-3 Áreas Verdes Proyectadas Comunales
- ICH Inmuebles de Conservación Histórica
- Zonas de Conservación Histórica

VIAS ESTRUCTURANTES

- Existentes
- Aperturas
- Ensanches
- Pasada a diferente Nivel
- Estaciones del Metro

ÁREAS DE PROTECCIÓN DE CANALES DE RIEGO (AR-1)

- Cauce Zanjón de la Aguada (3 m. desde cada borde)
- Cauce Canal San Joaquín (3 m. desde cada borde)

ÁREAS DE RESGUARDO DE AERODROMOS (AR-2)

- Límite Áreas Aeródromo El Bosque

ÁREAS DE RESGUARDO DE LINEAS DE ALTA TENSIÓN (AR-3)

- 20 Línea de Alta Tensión 110 KV y Área de Protección 20 m.

ÁREAS DE RESGUARDO VÍAS FÉRREAS (AR-4)

- F.F.C.C. de Circunvalación (20 m. a ambos lados)
- Línea Metro Subterránea

INFORMACIÓN GENERAL

- Límite Manzana
- División Predial y Solera
- Límite Urbano y Comunal
- Curvas de Nivel

FUENTE

BASE CARTOGRÁFICA
DATUM SAD69 - ELIPSOIDE INTERNACIONAL DE 1924

ESCALA

200 100 0 100 200

1:5.000

FECHA

LAMINA

1 de 2

CARTOGRAFÍA

SERVICIO AEROFOTOGRAMÉTRICO FUERZA AÉREA DE CHILE (SAF)

PROMULGACIÓN MUNICIPAL DE LA APROBACIÓN

EL SECRETARIO MUNICIPAL Y MINISTRO DE FE QUE SUSCRIBE, CERTIFICA QUE LA APROBACIÓN DE LA PRESENTE ENMIENDA DEL PRC DE LA COMUNA DE SAN MIGUEL FUE PROMULGADA POR DECRETO ALCALDICIO Nº 1889 DE FECHA 22/11/2006, PUBLICADO EN EL DIARIO OFICIAL DE____________.-

LUIS SANDOVAL GOMEZ
SECRETARIO MUNICIPAL

MINISTERIO DE VIVIENDA Y URBANISMO
SECRETARIA REGIONAL MINISTERIAL REGIÓN METROPOLITANA

INFORME TÉCNICO OFICIO ORD. Nº______________ DE FECHA_________________.-

VERONICA SERRANO MADRID
SECRETARIO REGIONAL MINISTERIAL
REGIÓN METROPOLITANA

JAVIER WOOD LARRAÍN
JEFE UNIDAD DE DESARROLLO URBANO
E INFRAESTRUCTURA

APROBACION MUNICIPAL

EL SECRETARIO MUNICIPAL Y MINISTRO DE FE QUE SUSCRIBE, CERTIFICA QUE LA PRESENTE ENMIENDA DEL PRC DE LA COMUNA DE SAN MIGUEL FUE APROBADO POR ACUERDOS DEL CONCEJO COMUNAL Nºs 829, 841, 842, 843, 844, 845, 846, 847, 848, 849, 850, 851, 852, 853, 854, 855 y 856 DE FECHAS 04.07.2006, 24.10.2006, 25.10.2006 y 30.10.2006; SANCIONADOS POR DECRETO ALCALDICIO Nº ______ DE FECHA ________

LUIS SANDOVAL GOMEZ
SECRETARIO MUNICIPAL

PEDRO GODOY LEÓN
ASESOR URBANISTA

JULIO PALESTRO VELÁSQUEZ
ALCALDE

IEN - LGL